


Perfiles Verticales de Asentamiento

Perfiles Verticales de Asentamiento

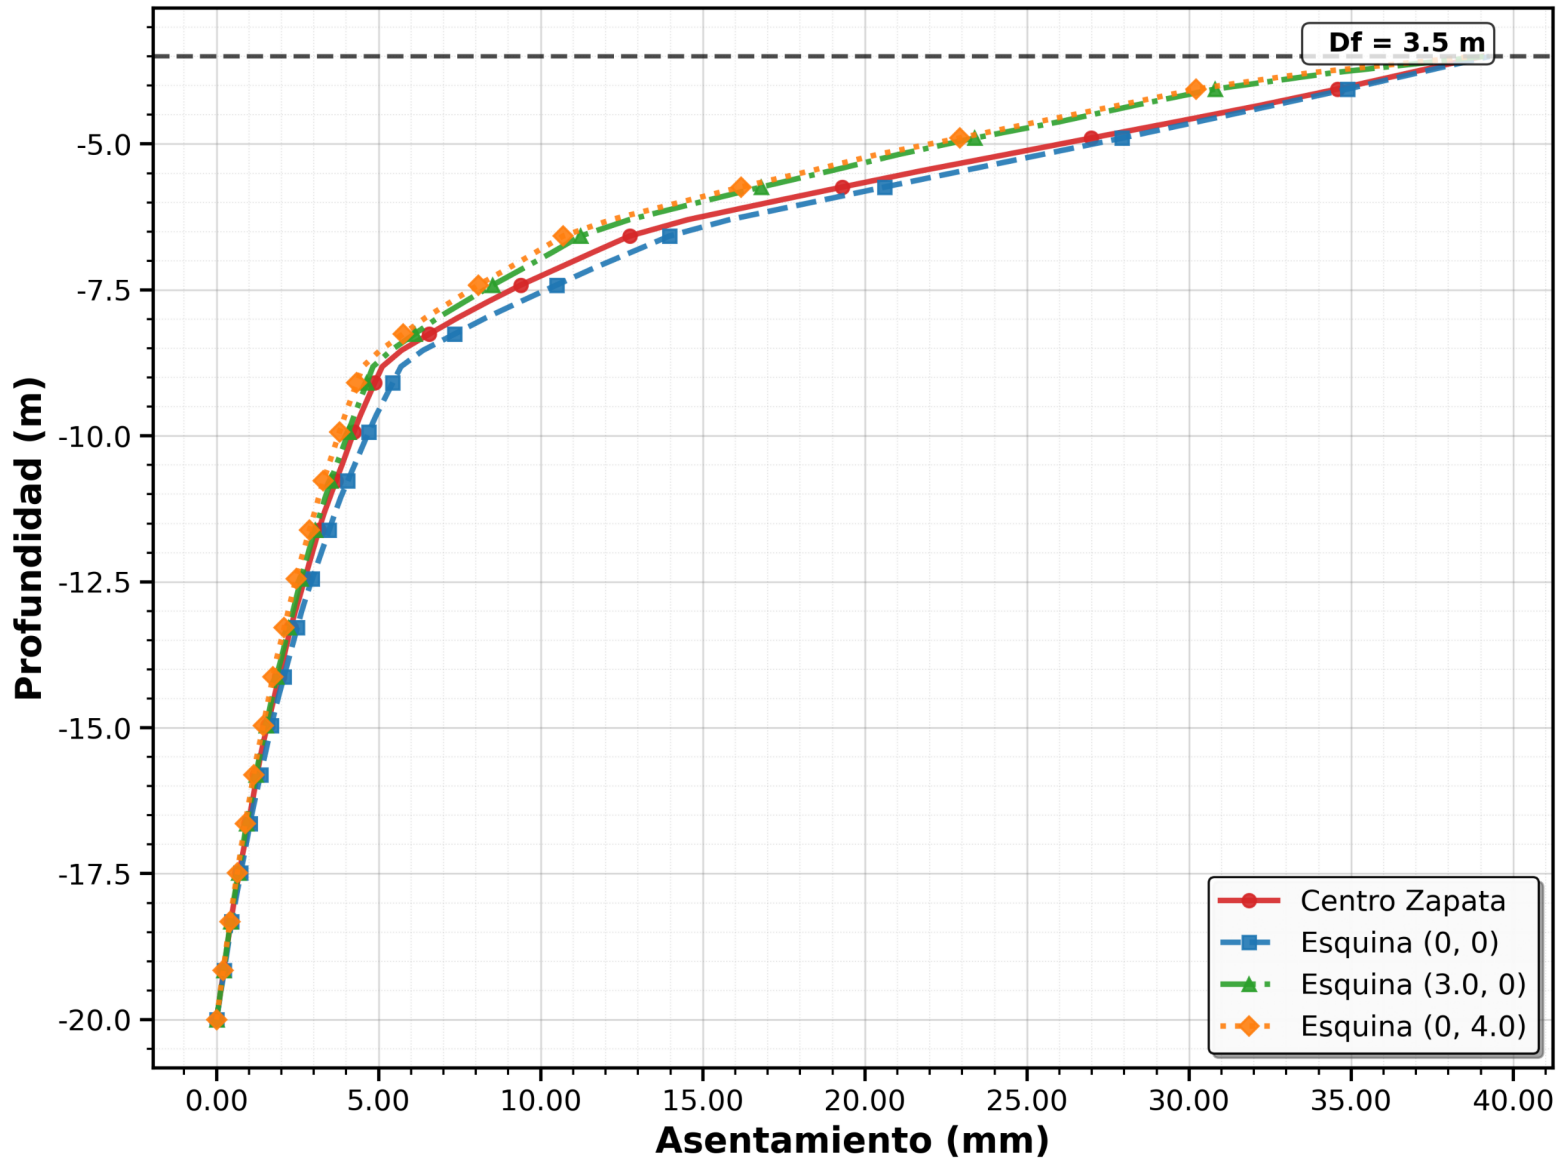

Variación del asentamiento con la profundidad en el centro y esquinas de la zapata