


Estratificación del Modelo

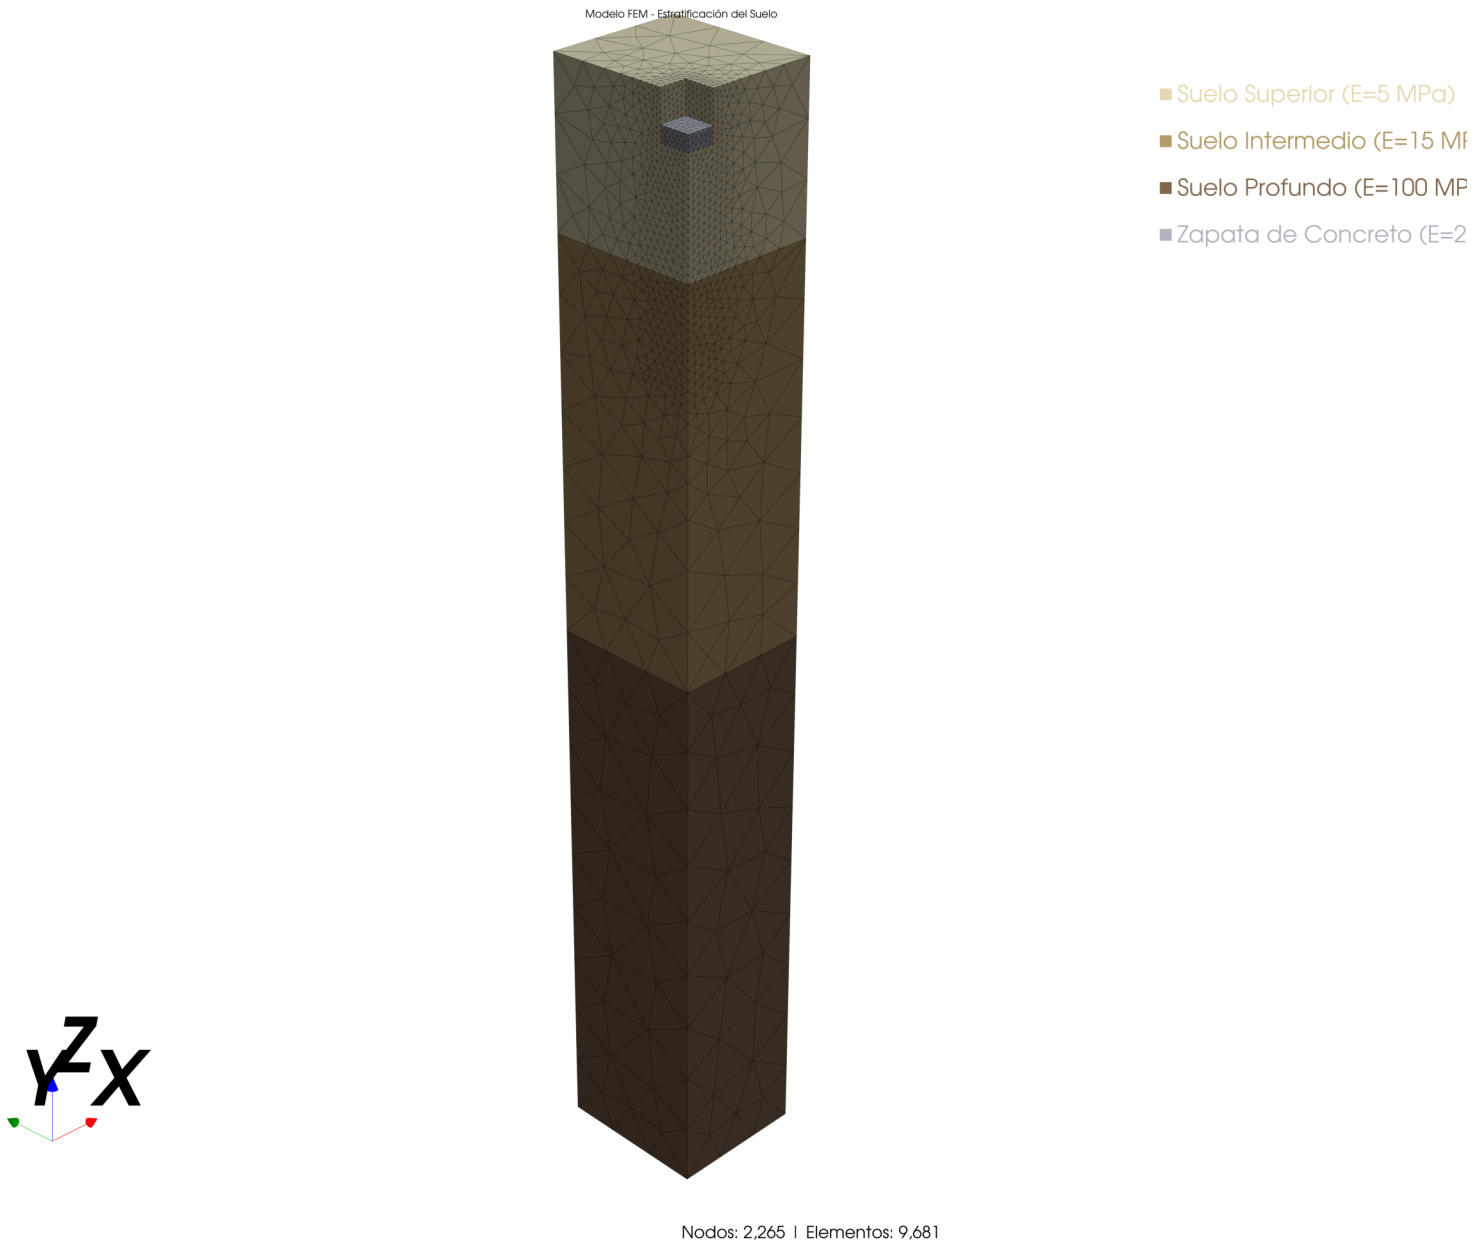

Vista isométrica mostrando los estratos de suelo y zapata de concreto